
PLANTA DO PISO 0

PROPOSTA DE RENOVAÇÃO · ESCALA 1:75 · COTAS EM METROS

LEGENDA
PAREDE EXISTENTE — ALVENARIA DE PEDRA (0,55 m)
PAREDE NOVA — TABIQUE / GESSO CARTONADO (0,12 m)
VÃO ENVIDRAÇADO
PORTA COM SENTIDO DE ABERTURA
PAVIMENTO EXTERIOR EM LAJETA DE GRANITO

QUADRO DE ÁREAS · PISO 0	
W.C.	6,00 m²
SALA / COZINHA	26,76 m²
LAVANDARIA	4,59 m²
ESCRITÓRIO	5,87 m²
ÁREA ÚTIL DO PISO 0	43,22 m²
QUINTAL (EXTERIOR)	17,27 m²

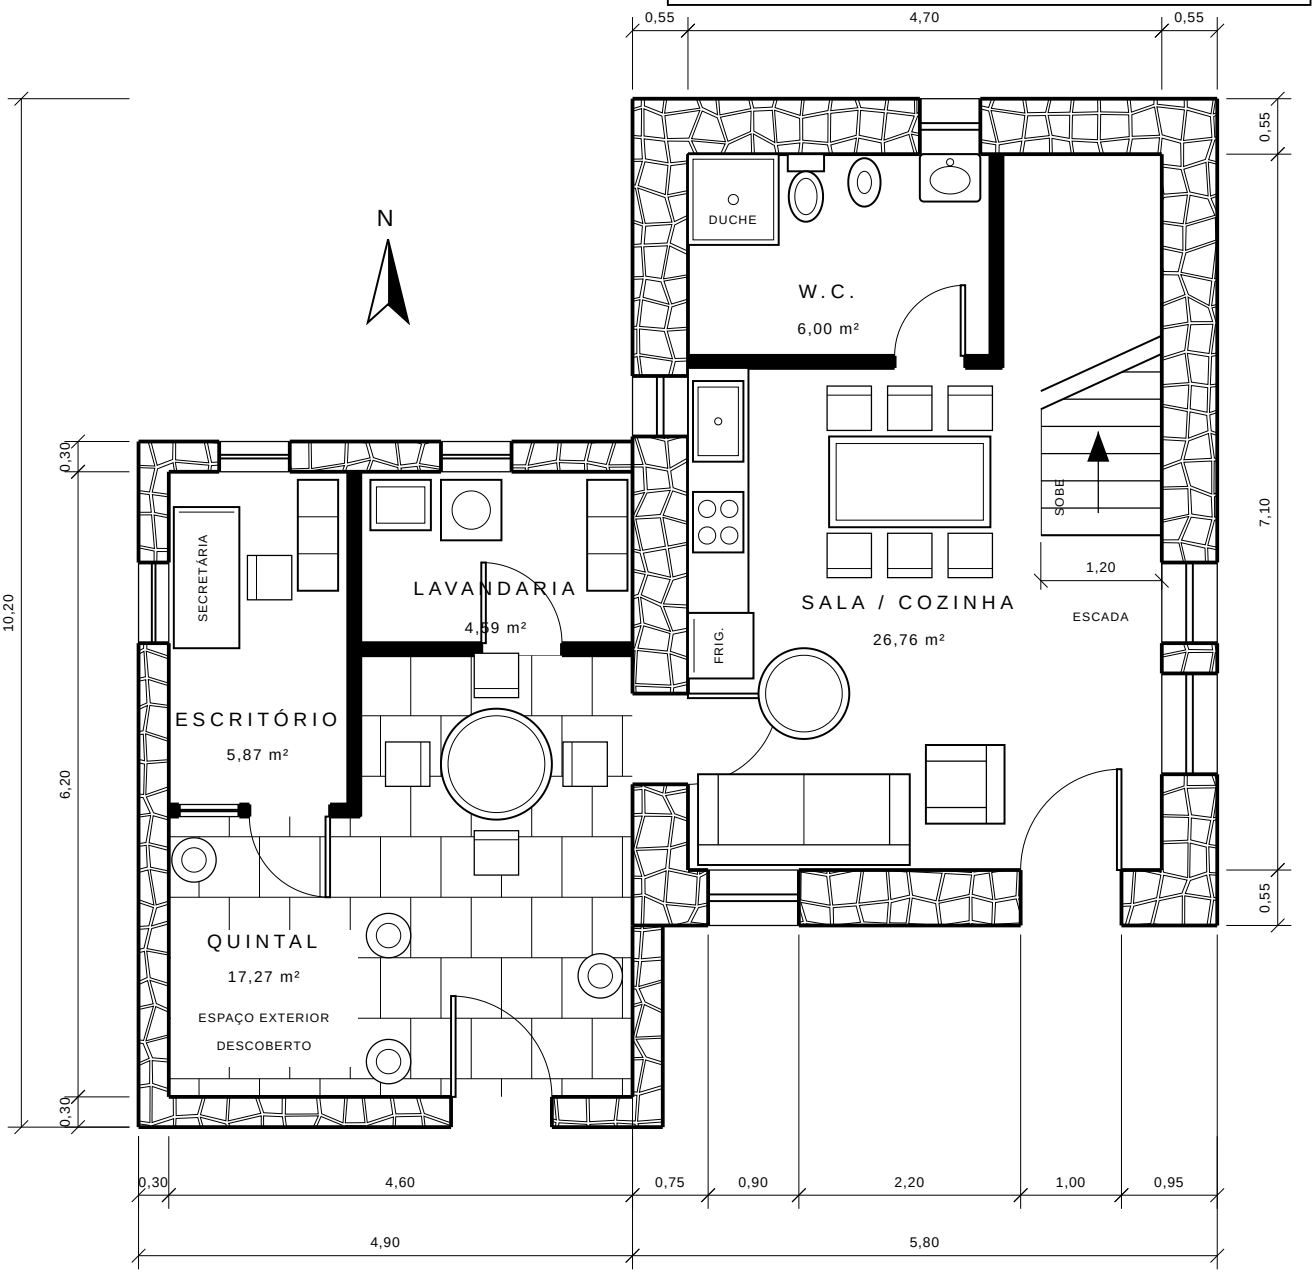

ESCALA 1:75 (m)

0 1 2 3 4 5

NOTAS

1. Cotas em metros, medidas em tosco. A confirmar em obra.
2. Paredes exteriores em alvenaria de pedra existente (0,55 m), a manter e consolidar.
3. Paredes interiores novas em tabique de madeira ou gesso cartonado (0,12 m).
4. Pé-direito do piso 0: 2,60 m sob o vigamento de madeira.
5. Escada em madeira maciça: 15 espelhos de 0,187 m e 14 cobertores de 0,27 m.
6. Vãos existentes a manter; novos vãos exigem lintel e verificação estrutural.

PROJECTO

CASA DE PEDRA

PROPOSTA DE RENOVAÇÃO · HABITAÇÃO UNIFAMILIAR T1

FASE ESTUDO PRÉVIO — PLANTAS DE ARQUITECTURA

DESENHO CONCEPTUAL. SUJEITO A LEVANTAMENTO RIGOROSO E A VALIDAÇÃO ESTRUTURAL DAS PAREDES EXISTENTES. NÃO ESCALAR O DESENHO.

DESENHO

PLANTA DO PISO 0

PROPOSTA

COTAS EM METROS

COTAS EM TOSCO

ESCALA 1:75

DATA 09.2026

FOLHA 01 DE 02

FORMATO A4